


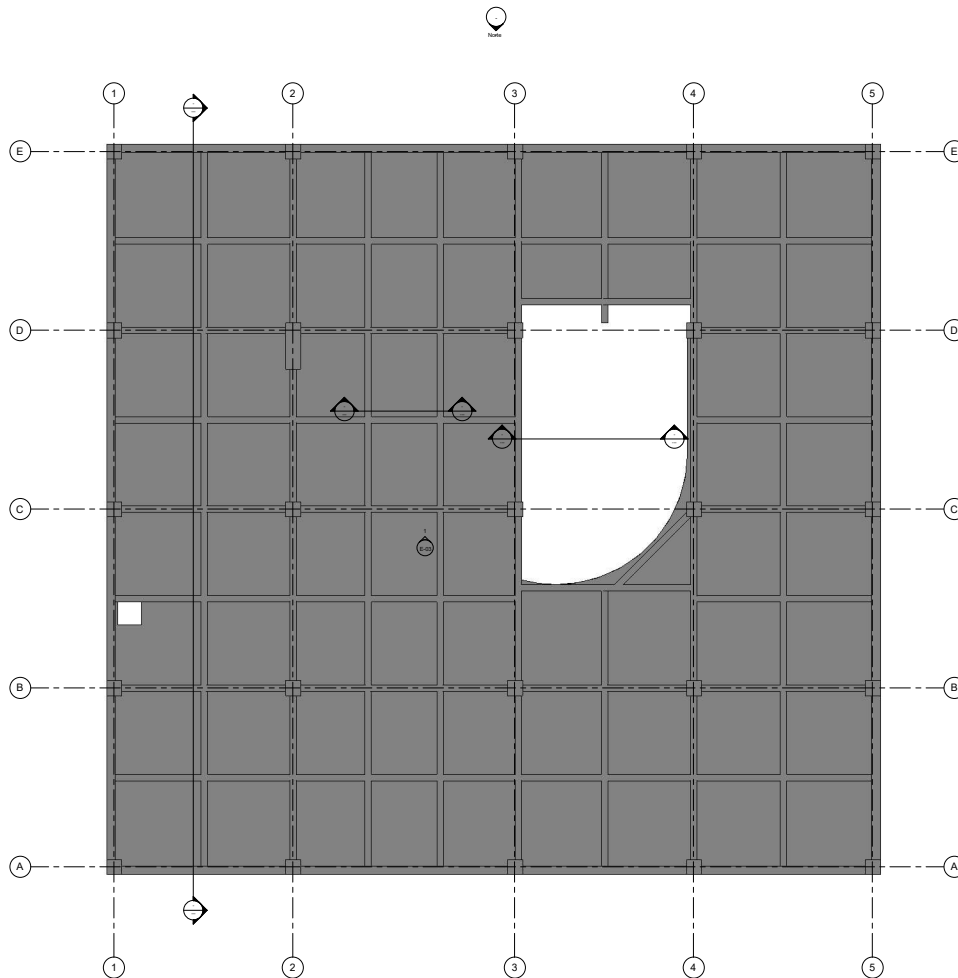

Losas macizas									
Nivel	Familia y tipo	Familia	Tipo	Recuento	Perímetro	Grosor de núcleo	Volumen	Área	Comentarios
Sótano 02	Suelo: Losa maciza e=0.15 m	Suelo	Losa maciza e=0.15 m	69	<variar>	0.150	138.96 m³	924 m²	<variar>
Sótano 01	Suelo: Losa maciza e=0.15 m	Suelo	Losa maciza e=0.15 m	69	<variar>	0.150	138.96 m³	924 m²	<variar>
Nivel 01	Suelo: Losa maciza e=0.15 m	Suelo	Losa maciza e=0.15 m	69	<variar>	0.150	138.96 m³	924 m²	<variar>
Nivel 02	Suelo: Losa maciza e=0.15 m	Suelo	Losa maciza e=0.15 m	65	<variar>	0.150	90.09 m³	601 m²	<variar>
Nivel 03	Suelo: Losa maciza e=0.15 m	Suelo	Losa maciza e=0.15 m	66	<variar>	0.150	90.09 m³	601 m²	<variar>
Techo	Suelo: Losa maciza e=0.15 m	Suelo	Losa maciza e=0.15 m	66	<variar>	0.150	90.09 m³	601 m²	<variar>
Total general: 375							685.96 m³	4573 m²	

Vigas de concreto					
Nivel de referencia	Tipo	Recuento	Longitud	Volumen	Comentarios
Sótano 02	V - 0.30x0.5 m	34	280.907	39.68 m³	
Sótano 02	V - 0.30x0.7 m	10	121.202	23.04 m³	
Sótano 02	V - 0.30x0.9 m	10	98.850	22.21 m³	
Sótano 01	V - 0.30x0.5 m	34	280.907	39.68 m³	
Sótano 01	V - 0.30x0.7 m	10	121.202	23.04 m³	
Sótano 01	V - 0.30x0.9 m	10	98.850	22.21 m³	
Nivel 01	V - 0.30x0.5 m	34	280.907	39.68 m³	
Nivel 01	V - 0.30x0.7 m	10	121.202	23.04 m³	
Nivel 01	V - 0.30x0.9 m	10	98.850	22.21 m³	
Nivel 02	V - 0.30x0.5 m	32	180.104	25.44 m³	
Nivel 02	V - 0.30x0.7 m	10	116.363	22.21 m³	
Nivel 02	V - 0.30x0.9 m	3	14.123	6.63 m³	
Nivel 02	V - 0.60x1.20 m	1	11.738	6.62 m³	
Nivel 02	V - 0.60x1.20 m	1	4.000	1.08 m³	
DE			444.718	60.99 m³	
Nivel 03	V - 0.30x0.5 m	32	180.104	25.44 m³	
Nivel 03	V - 0.30x0.7 m	10	116.363	22.21 m³	
Nivel 03	V - 0.30x0.9 m	3	14.123	6.63 m³	
Nivel 03	V - 0.60x1.20 m	1	11.738	6.62 m³	
Techo	V - 0.30x0.5 m	32	180.104	25.44 m³	
Techo	V - 0.30x0.7 m	10	116.363	22.21 m³	
Techo	V - 0.30x0.9 m	3	14.123	6.63 m³	
Techo	V - 0.60x1.20 m	1	11.738	6.62 m³	
Total general: 343			2799.653	511.50 m³	

1 Encofrado Sótano 03
1:75



Nombre de lámina:

Encofrado sótano 03

Nombre del proyecto: Proyecto Comercial - Konstruedu

Nombre de proyecto: 2021-001

Nombre del cliente: Konstruedu

Escala: 1:75

Fecha de emisión: 01/06/24

Revisión:

Diseñado por: Autor

Revisado por: Verificador

Aprobado por: Autorizador

Lámina:

E-02