


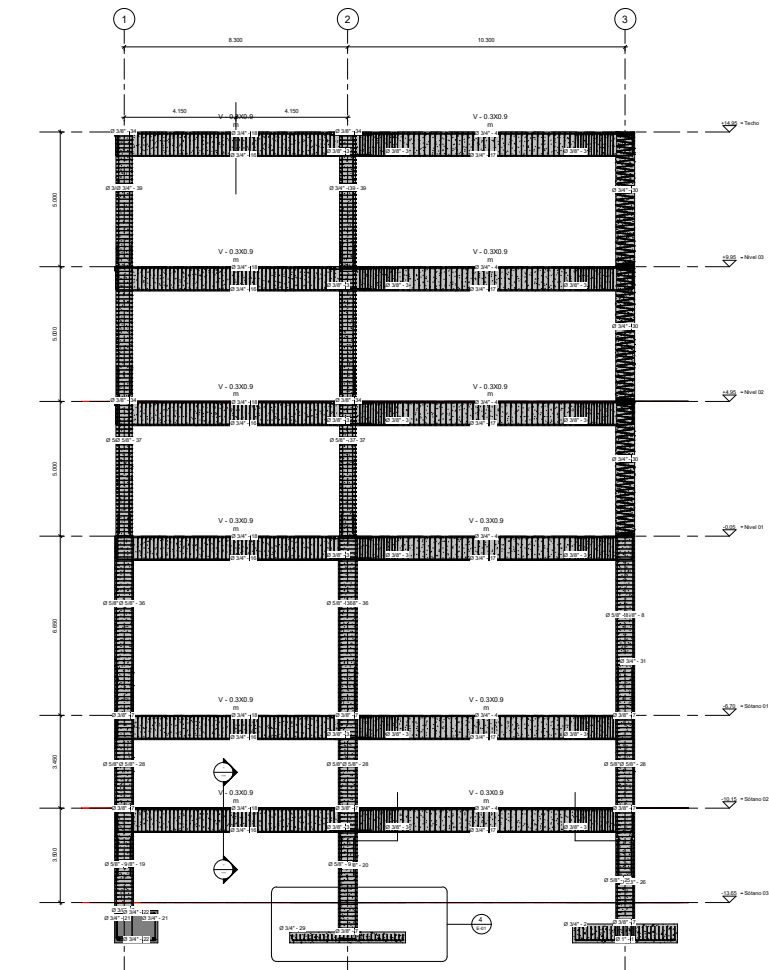

1 Alzado 1 - a
1 : 60

3 3D Acero



Nombre de la lámina:

Pórtico

Nombre del proyecto: Proyecto Comercial - Konstruedu
Número de proyecto: 2021-001
Nombre del cliente: Konstruedu


Escala: 1 : 60
Fecha de emisión: 01/06/24
Revisión:

Diseñado por: Carlos Andres Niño Mosquera
Revisado por: Carlos Andres Niño Mosquera
Aprobado por: Carlos Andres Niño Mosquera

Lámina:

E-03

Tabla de Acero de refuerzo				
Categoría de refuerzo	Dámetro de barra	Longitud de barra	Cantidad	Peso Nominal
Armazón estructural	18"	varia	varia	0.58 kg/m
Armazón estructural	14"	varia	3	2.24 kg/m
Concreción estructural	14"	varia	varia	2.24 kg/m
Concreción estructural	1"	4.68	26	3.97 kg/m
Concreción estructural	12"	varia	varia	0.99 kg/m
Pilar estructural	18"	1.64	varia	0.95 kg/m
Pilar estructural	18"	varia	3	1.55 kg/m
Pilar estructural	14"	varia	varia	2.24 kg/m
Bele	18"	varia	varia	0.58 kg/m

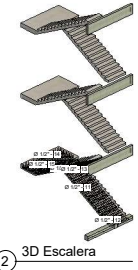

2 3D Escalera

